

Project Title	HDFC Bank, Madipakkam, Chennai. – Tactile Installation
----------------------	--

Project Date	02 August 2025
---------------------	----------------

Overview

The project involves conducting a site survey, preparing a 2D design, and installing PU tactile pathways at HDFC Bank, Madipakkam, to enhance accessibility and ensure safe navigation for persons with visual impairments.

The work was executed as per the Harmonised Guidelines, ensuring safe and barrier-free movement for persons with visual impairments.

Photos




MD	1050 X 2100	TOU. GLASS MAIN DOOR
D1	900 X 2100	TOU. GLASS DOOR
D2	750 X 2100	SOLID FLUSH DOOR WITH VISION PANEL
D3	750 X 2100	SOLID FLUSH DOOR WITH AIR VENT GRILL
D4	1050 X 2100	SOLID FLUSH DOOR WITH VISION PANEL
D5	825 X 2100	SOLID FLUSH DOOR WITH VISION PANEL
D6	900 X 2100	SOLID FLUSH DOOR WITH VISION PANEL
WK	675 X 1200	WICKET DOOR

NOTE:

	PRO. 7' HT GLAZED PARTITION
	EXISTING 3" FULL HT SOLID PARTITION
	PROPOSED 3" FULL HT SOLID PARTITION
	PROPOSED 3" FULL HT SEMI GLAZED PARTITION
	PROPOSED 3" FULL HT FIRE RATED PARTITION
	EXISTING 3" HALF HT PARTITION
	PROPOSED 3" HALF HT PARTITION
	EXISTING - BRICK WALL
	PROPOSED 4.5" BRICK WALL
	PROPOSED 6" BRICK WALL
	EXISTING - R.C.C WALL
	PROPOSED STORAGE

CARPET AREA STATEMENT	SQ FT	SQ MT
ATM AREA	64.06	5.95
GROUND FLOOR AREA	1425.31	132.41
FIRST FLOOR AREA	830.90	77.19
TOTAL CARPET AREA	<u>2320.27</u>	<u>215.56</u>
GF - STAIRCASE AREA	57.00	5.30
FF - STAIRCASE AREA	60.20	5.59
STAIRCASE AREA	<u>117.20</u>	<u>10.89</u>

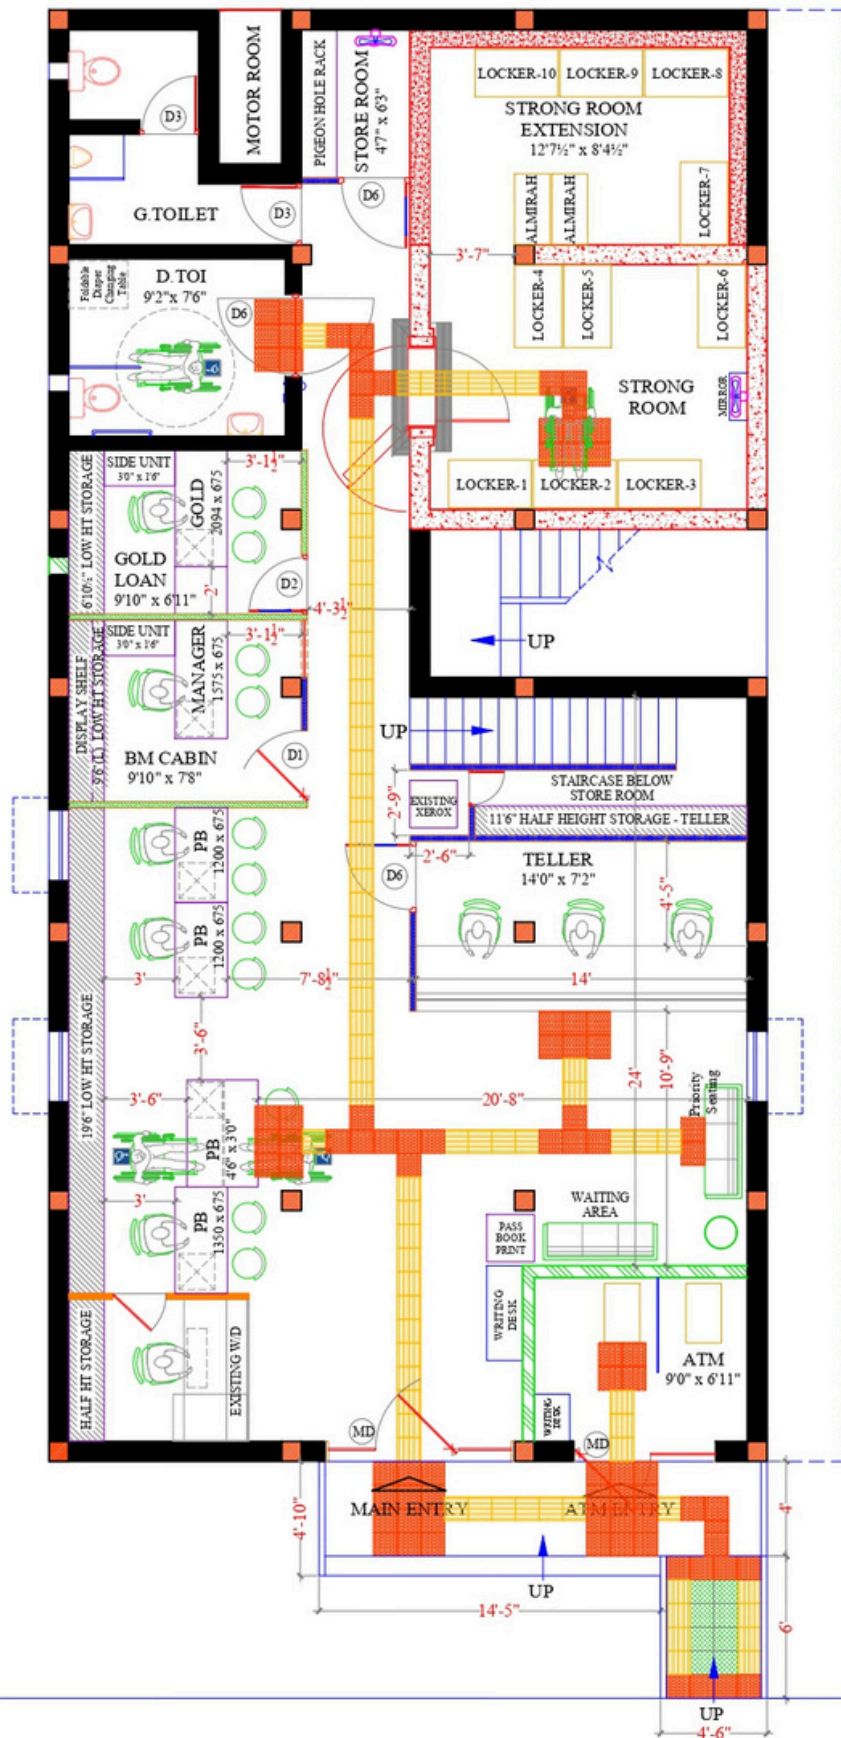

PROJECT NAME:
INTERIOR DESIGN
CLIENT NAME:
HDFC BANK
PLACE OF THE PROJECT:
MADIPPAKKAM, CHENNAI.

TITLE:-
**PROPOSED
GROUND FLOOR
INTERIOR LAYOUT**
A3-FORMAT-II. 7"x16.5"

SCALE : 1" = 8'6"
DATE : 12-06-2025
DRN BY:
DRG NO: SCH-11B-GF
JOB NO:
CHK BY:

Aabak Engineers Inc
NO.58 A.V.CHURCH ROAD,
BESANT NAGAR, CHENNAI-90.
CONTACT: 9841720600.